


Nr	Y	X	H	Kodi	Përshkrimi	Burimi
8	7512567.708	4693420.511	623.250	40	Shtëpi-Ndërtesë	PM
9	7512566.818	4693412.642	623.250	40	Shtëpi-Ndërtesë	PM
10	7512566.458	4693410.963	623.250	40	Shtëpi-Ndërtesë	PM
11	7512567.639	4693409.133	623.250	40	Shtëpi-Ndërtesë	PM
12	7512566.927	4693416.722	623.250	40	Shtëpi-Ndërtesë	PM
13	7512564.962	4693415.429	623.250	40	Shtëpi-Ndërtesë	PM
14	7512570.896	4693408.576	623.250	40	Shtëpi-Ndërtesë	PM
15	7512570.628	4693406.883	623.250	40	Shtëpi-Ndërtesë	PM
47	7512579.602	4693418.194	623.250	40	Shtëpi-Ndërtesë	PM
50	7512577.609	4693407.345	623.250	40	Shtëpi-Ndërtesë	PM
51	7512574.097	4693407.982	623.250	40	Shtëpi-Ndërtesë	PM
56	7512573.750	4693406.277	623.250	40	Shtëpi-Ndërtesë	PM

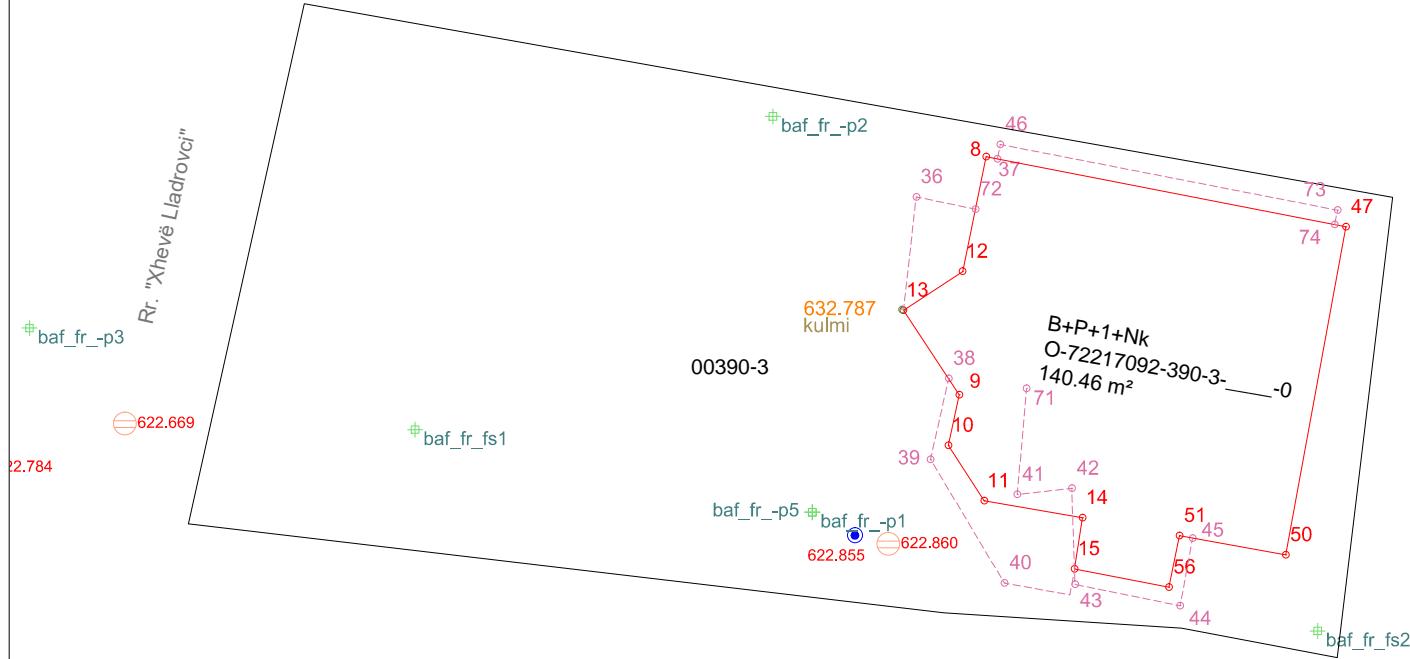

Republika e Kosovës

Qeveria - Vlada

Ministria e Mjedisit dhe Planifikimit Hapësinor /Ministarstv Sredine i Prstrin Planiranja
AGJENCIJA KADASTRALE E KOSOVËS/ KATASTARSKA AGENCIJA KOSOVA

Situacioni i terrenit

Zyra kadastrale kmunale / pëtinska katastarska kancelarija: Ferizaj

Zona kadastrale / Katastarska zona: Ferizaj

Nr. i njësisë kadastrale / Br. katastarske jedinice : 00390-3

Numri i lëndës / Broj predmeta:

Shkalla e zvoglimit / Razmera plana 1: 250

Lista e koordinatave të pikave të matura:

Nr	Y	X	H	DSC
64	7512548.830	4693411.491	624.373	baf_fr_fs1
65	7512578.667	4693404.834	624.297	baf_fr_fs2
66	7512561.959	4693408.762	622.798	baf_fr_p1
67	7512560.657	4693421.843	622.699	baf_fr_p2
68	7512536.083	4693414.844	622.693	baf_fr_p3
69	7512581.978	4693435.219	622.504	baf_fr_p4
70	7512561.960	4693408.756	622.803	baf_fr_p5
35	7512564.921	4693415.457	632.787	/kulmi
1	7512563.367	4693407.990	622.855	kyqe_uj
8	7512567.703	4693420.511	623.250	perdhese
9	7512566.818	4693412.642	623.250	perdhese
10	7512566.458	4693410.963	623.250	perdhese
11	7512567.639	4693409.133	623.250	perdhese
12	7512566.927	4693416.722	623.250	perdhese
13	7512564.962	4693415.429	623.250	perdhese
14	7512570.898	4693408.576	623.250	perdhese
15	7512570.628	4693406.883	623.250	perdhese
47	7512579.602	4693418.194	623.250	perdhese
50	7512577.609	4693407.345	623.250	perdhese
51	7512574.097	4693407.982	623.250	perdhese
56	7512573.750	4693406.277	623.250	perdhese

Shpjegues:

Kufiri kadastral (nga SIKTK-G)

■ Ndërtesa në trajtim për legalizim

Ndërtesa tjera

Aneks Ndërtimi

■ Shtyllë elektrike

● Pusetë e ujësjellësit

○ Pusetë e ujërave të zeza

□ Strehët

④ Kyqje në rrymë

Rilevoi / Snimi: LIRIDON SEJDIU

(emri dhe mbiemri i gjedhit/kompanisë/ ime i prezime gedeta/ kompanije)

Nr. i licencës / Br. licence: 140

Data e rilevimit / Datum snimanja: 04.09.2025

Nënshkrimi / Potpis: _____

V.V.

Pikë e objekteve fqinje

Rr. Emri i rrugës

Pikë e rrjetës gjeodezike

Pikë e strehëve

Pikë e terasës

Pikë e objektit

Pikë e murit

Pikë e kulmit

Nr	Y	X	H	Kodi	Përvkrimi	Burimi
8	7512567.708	4693420.511	623.250	40	Shtëpi-Ndërtesë	PM
9	7512566.818	4693412.642	623.250	40	Shtëpi-Ndërtesë	PM
10	7512566.458	4693410.963	623.250	40	Shtëpi-Ndërtesë	PM
11	7512567.639	4693409.133	623.250	40	Shtëpi-Ndërtesë	PM
12	7512566.927	4693416.722	623.250	40	Shtëpi-Ndërtesë	PM
13	7512564.962	4693415.429	623.250	40	Shtëpi-Ndërtesë	PM
14	7512570.896	4693408.576	623.250	40	Shtëpi-Ndërtesë	PM
15	7512570.628	4693406.883	623.250	40	Shtëpi-Ndërtesë	PM
47	7512579.602	4693418.194	623.250	40	Shtëpi-Ndërtesë	PM
50	7512577.609	4693407.345	623.250	40	Shtëpi-Ndërtesë	PM
51	7512574.097	4693407.982	623.250	40	Shtëpi-Ndërtesë	PM
56	7512573.750	4693406.277	623.250	40	Shtëpi-Ndërtesë	PM



Republika e Kosovës

Qeveria - Vlada



Ministria e Mjedisit dhe Planifikimit Hapësinor /Ministarstv Sredine i Prstrg Planiranja
AGJENCIJA KADASTRALE E KOSOVËS/ KATASTARSKA AGJENCIJA KOSOVA

Situacioni i terrenit

Orto 2018

Zyra kadastrale kmunale / pëtinska katastarska kancelarija: Ferizaj

Zona kadastrale / Katastarska zona: Ferizaj

Nr. i njësisë kadastrale / Br. katastarske jedinice : 00390-3

Numri i lëndës / Broj predmeta:

Shkalla e zvoglimit / Razmera plana 1: 250

Lista e koordinatave të pikave të matura:

Nr	Y	X	H	DSC
64	7512548.830	4693411.491	624.373	baf_fr_f1
65	7512578.667	4693404.834	624.297	baf_fr_f2
66	7512561.959	4693408.762	622.798	baf_fr_p1
67	7512560.657	4693421.843	622.699	baf_fr_p2
68	7512536.083	4693414.844	622.693	baf_fr_p3
69	7512581.978	4693435.219	622.504	baf_fr_p4
70	7512561.960	4693408.756	622.803	baf_fr_p5
35	7512564.921	4693415.457	632.787	/kulmi
1	7512563.367	4693407.990	622.858	kyqe_uj
8	7512567.703	4693420.511	623.250	perdhese
9	7512566.818	4693412.642	623.250	perdhese
10	7512566.458	4693410.963	623.250	perdhese
11	7512567.639	4693409.133	623.250	perdhese
12	7512566.927	4693416.722	623.250	perdhese
13	7512564.962	4693415.429	623.250	perdhese
14	7512570.896	4693408.576	623.250	perdhese
15	7512570.628	4693406.883	623.250	perdhese
47	7512579.602	4693418.194	623.250	perdhese
50	7512577.609	4693407.345	623.250	perdhese
51	7512574.097	4693407.982	623.250	perdhese
56	7512573.750	4693406.277	623.250	perdhese

Shpjegues:

Kufiri kadastral (nga SIKTK-G)

■ Ndërtesa në trajtim për legalizim

Ndërtesa tjera

Aneks Ndërtimi

▲ Shtyllë elektrike

● Pusetë e ujësjellësit

○ Pusetë e ujërave të zeza

□ Strehët

◎ Kyqje në rrymë

Rilevoi / Snimi: LIRIDON SEJDIU

(emri dhe mbiemri i gjedjetit/kompanisë/ ime i prezime gedeta/ kompanije)

Nr. i licencës / Br. licence: 140

Data e rilevimit / Datum snimanja: 04.09.2025

Nënshkrimi / Potpis: _____

V.V.

Pikë e objekteve fqinje

Rr. Emri i rrugës

Pikë e rrjetës gjeodezike

Pikë e strehëve

Pikë e terasës

Pikë e objektit

Pikë e murit

Pikë e kulmit

81

10

□

●

○

◎



Republika e Kosovës
Republika Kosova-Republic of Kosovo
Qeveria e Kosovës- Vlada Kosova- Government of Kosovo
Ministria e Infrastrukturës dhe Ambientit/ Ministrastvo Infrastrukture i Sredine/ Ministry of Infrastructure and Environment
AGJENCIA KADASTRALE E KOSOVËS/KOSOVSKA KATASTARSKA AGENCIJA/ KOSOVO CADASTRAL AGENCY

Komuna: Ferizaj

Numri i njësis kadastrale: 00390-3

Zona Kadastrale: Ferizaj

Sistemi koordinat: KosovaRef01

Nr	Y	X	H	Kodi	Përshkrimi	Burimi
8	7512567.708	4693420.511	623.250	40	Shtëpi-Ndërtesë	PM
9	7512566.818	4693412.642	623.250	40	Shtëpi-Ndërtesë	PM
10	7512566.458	4693410.963	623.250	40	Shtëpi-Ndërtesë	PM
11	7512567.639	4693409.133	623.250	40	Shtëpi-Ndërtesë	PM
12	7512566.927	4693416.722	623.250	40	Shtëpi-Ndërtesë	PM
13	7512564.962	4693415.429	623.250	40	Shtëpi-Ndërtesë	PM
14	7512570.896	4693408.576	623.250	40	Shtëpi-Ndërtesë	PM
15	7512570.628	4693406.883	623.250	40	Shtëpi-Ndërtesë	PM
47	7512579.602	4693418.194	623.250	40	Shtëpi-Ndërtesë	PM
50	7512577.609	4693407.345	623.250	40	Shtëpi-Ndërtesë	PM
51	7512574.097	4693407.982	623.250	40	Shtëpi-Ndërtesë	PM
56	7512573.750	4693406.277	623.250	40	Shtëpi-Ndërtesë	PM

Gjeodeti / Kompania gjeodete e licencuar:	Liridon Sejdiu	Nënshkrimi dhe vula:	
Numri i licencës	140		

Kérko

Rezultati i kërkimit

Shfaq Zgjedhur Rezultatet Shkarko

ParcelDetailId	CadastreUnitId	CadastreZoneId	Ca
11157771	P-72217092-00...	72217092	72

Lista e shtresës Ndhima

- Ortofoto
 - Orthophoto2024Rural
 - Orthophoto2024Urban
 - Orthophoto2018Rural
 - Orthophoto2018Malore
 - Orthophoto2018Urban
 - Ortofoto 2015 UAV
 - Ortofoto 2012
 - Ortofoto 2009
 - Ortofoto 2004
- Hartat Topografike
 - Harta Topografike 1:250000
 - Harta Topografike 1:25000 (2015)
 - Nomenklatura
- Rindërtimi i Informacioneve Kadastrale
 - RIK_2025
- Modeli Dixhital i Terrenit
 - Modeli Dixhital i Terrenit
- Rilevimi
 - Indeksi i Ortofotove Rurale 2024
 - Indeksi i Ortofotove Urbane 202
 - Indeksi i Ortofotove 2018
- Rrjeti Rrugor
 - Autostradë
 - Rrugë Nacionale
 - Rrugë Rajonale
- Njësi Administrativë
 - Kufiri Shtetëror
 - Kufijtë dhe Emrat e Komunave
 - Zonë urbane
- Njësítë Kadastrale
 - Zonat Kadastrale
 - Parcelat
 - Numri parcelës
 - Ndërtesat
 - Numri ndërtesës
- Sistemi i Adresave
 - Rrugët

1 : 250

SIP RELA

MUSTAFË XHIGOLI

00390-2

00389-2

06

08

00390-1

Rugët

5-5

02872-1

663-0

Scale = 1 : 250

Pozita: 7512558.980, 4693421.580

KosovaRef01

Raport

Zyra kadastrale komunale / Opštinska katastarska kancelarija: FerizajNr. i njësisë kadastrale / Br. katastarske jedinice : 00390-3Zona kadastrale / Katastarska zona: Ferizaj

Numri i lëndës / Broj predmeta: _____

Lloji i njësisë kadastrale / Vrsta katastarske jedinice : ShtëpiShkalla e zvoglimit / Razmera plana 1: 250**Republika e Kosovës****Republika Kosova-Republic of Kosovo****Qeveria -Vlada-Government****Ministria e Mjedisit dhe Planifikimit Hapësinor /Ministarstvo Sredine i Prostornog Planiranja/Ministry of Environment and Spatial Planning**


AGJENCIA KADASTRALE E KOSOVËS/KATASTARSKA AGECIJA KOSOVA/KOSOVA CADASTRAL AGENCY



Rr. "Xhevë Lladrovci"

00390-3

Bodrumi
O-72217092-390-3-
140.46 m²

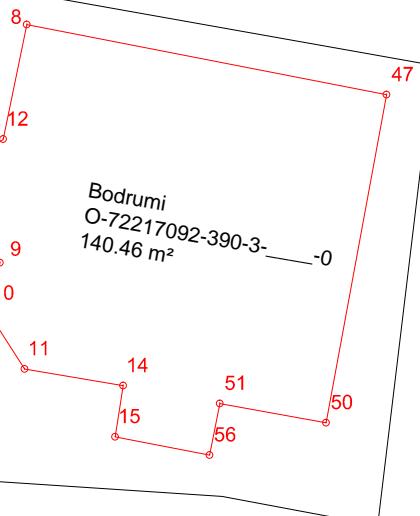

Nr.	Y	X	H	D	Etazhi	Sqarim	Sipërfaqja (m ²)
8	7512567.71	4693420.51	620.54	Bodrumi	Bodrumi	Bodrumi	140.46
9	7512566.82	4693412.64	620.54	Bodrumi			
10	7512566.46	4693410.96	620.54	Bodrumi			
11	7512567.64	4693409.13	620.54	Bodrumi			
12	7512566.93	4693416.72	620.54	Bodrumi			
13	7512564.96	4693415.43	620.54	Bodrumi			
14	7512570.90	4693408.58	620.54	Bodrumi			
15	7512570.63	4693406.88	620.54	Bodrumi			
47	7512579.60	4693418.19	620.54	Bodrumi			
50	7512577.61	4693407.35	620.54	Bodrumi			
51	7512574.10	4693407.98	620.54	Bodrumi			
56	7512573.75	4693406.28	620.54	Bodrumi			
						Gjithsej:	140.46

Rilevoi / Snimio: LIRIDON SEJDIU
(emri dhe mbiemri i gjyqetarit/kompanisë/ ime i prezime geodeta/ kompanije)Aprovoi / Usvojio: _____
(emri dhe mbiemri i pësonit zyrtar/ ime i prezime sluzbeneg lica)Nr. i licencës / Br. licence: 140

V.V.

Nënshkrimi / Potpis: _____

Nënshkrimi / Potpis: _____

Data e rilevimit / Datum snimanja: 04.09.2025

Data e rilevimit / Datum snimanja: _____

Zyra kadastrale komunale / Opštinska katastarska kancelarija: FerizajNr. i njësisë kadastrale / Br. katastarske jedinice : 00390-3Zona kadastrale / Katastarska zona: Ferizaj

Numri i lëndës / Broj predmeta: _____


Lloji i njësisë kadastrale / Vrsta katastarske jedinice : ShtëpiShkalla e zvoglimit / Razmera plana 1: 250

Republika e Kosovës
Republika Kosova-Republic of Kosovo
Qeveria -Vlada-Government

Ministria e Mjedisit dhe Planifikimit Hapësinor /Ministarstvo Sredine i Prostornog Planiranja/Ministry of Environment and Spatial Planning
 AGJENCIA KADASTRALE E KOSOVËS/KATASTARSKA AGECIJA KOSOVA/KOSOVA CADASTRAL AGENCY



Rr. "Xheivë Lladrovci"

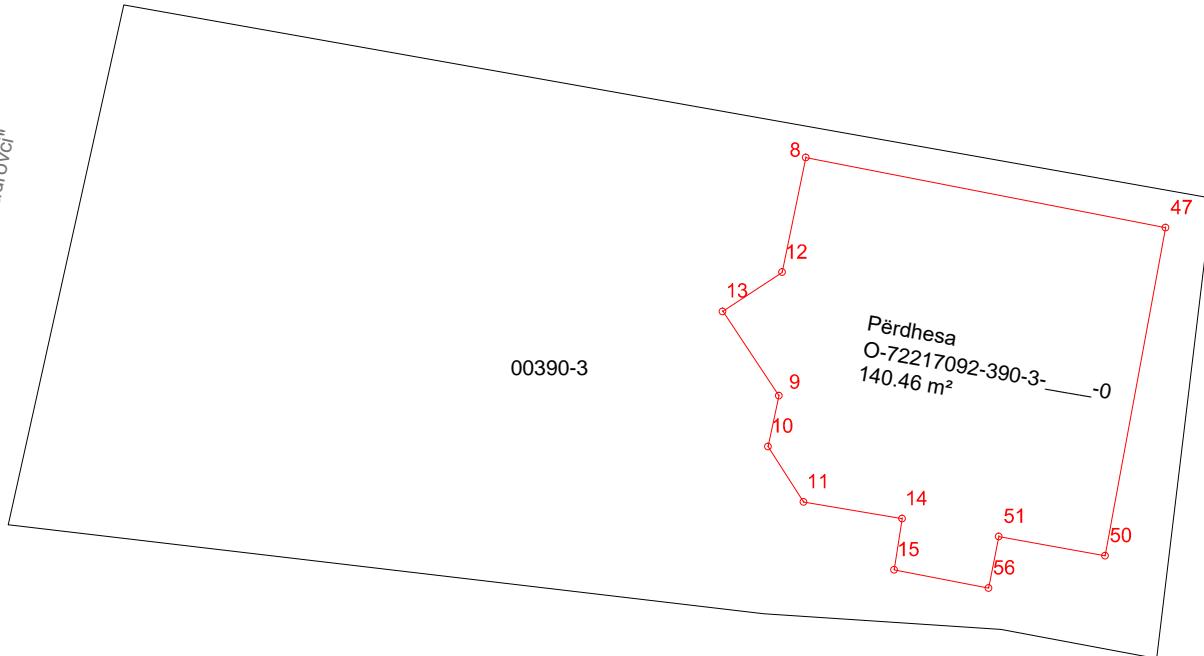

00390-3

Përdhesa
 O-72217092-390-3-
 140.46 m²

Nr.	Y	X	H	D	Etazhi	Sqarim	Sipërfaqja (m ²)
8	7512567.71	4693420.51	623.25	perdhese	Përdhesa	Përdhesa	140.46
9	7512566.82	4693412.64	623.25	perdhese			
10	7512566.46	4693410.96	623.25	perdhese			
11	7512567.64	4693409.13	623.25	perdhese			
12	7512566.93	4693416.72	623.25	perdhese			
13	7512564.96	4693415.43	623.25	perdhese			
14	7512570.90	4693408.58	623.25	perdhese			
15	7512570.63	4693406.88	623.25	perdhese			
47	7512579.60	4693418.19	623.25	perdhese			
50	7512577.61	4693407.35	623.25	perdhese			
51	7512574.10	4693407.98	623.25	perdhese			
56	7512573.75	4693406.28	623.25	perdhese			
					Gjithsej:		140.46

Rilevoi / Snimio: LIRIDON SEJDIU
 (emri dhe mbiemri i gjyqetit/kompanisë/ ime i prezime geodeta/ kompanije)Aprovoi / Usvojio: _____
 (emri dhe mbiemri i pësonit zyrtar/ ime i prezime sluzbeneg lica)Nr. i licencës / Br. licence: 140

V.V.

Nënshkrimi / Potpis: _____

Nënshkrimi / Potpis: _____

Data e rilevimit / Datum snimanja: 04.09.2025


Data e rilevimit / Datum snimanja: _____

Zyra kadastrale komunale / Opštinska katastarska kancelarija: FerizajNr. i njësisë kadastrale / Br. katastarske jedinice : 00390-3Zona kadastrale / Katastarska zona: Ferizaj

Numri i lëndës / Broj predmeta: _____

Lloji i njësisë kadastrale / Vrsta katastarske jedinice : ShtëpiShkalla e zvoglimit / Razmera plana 1: 250**Republika e Kosovës****Republika Kosova-Republic of Kosovo****Qeveria -Vlada-Government****Ministria e Mjedisit dhe Planifikimit Hapësinor /Ministarstvo Sredine i Prostornog Planiranja/Ministry of Environment and Spatial Planning**

AGJENCIA KADASTRALE E KOSOVËS/KATASTARSKA AGECIJA KOSOVA/KOSOVA CADASTRAL AGENCY

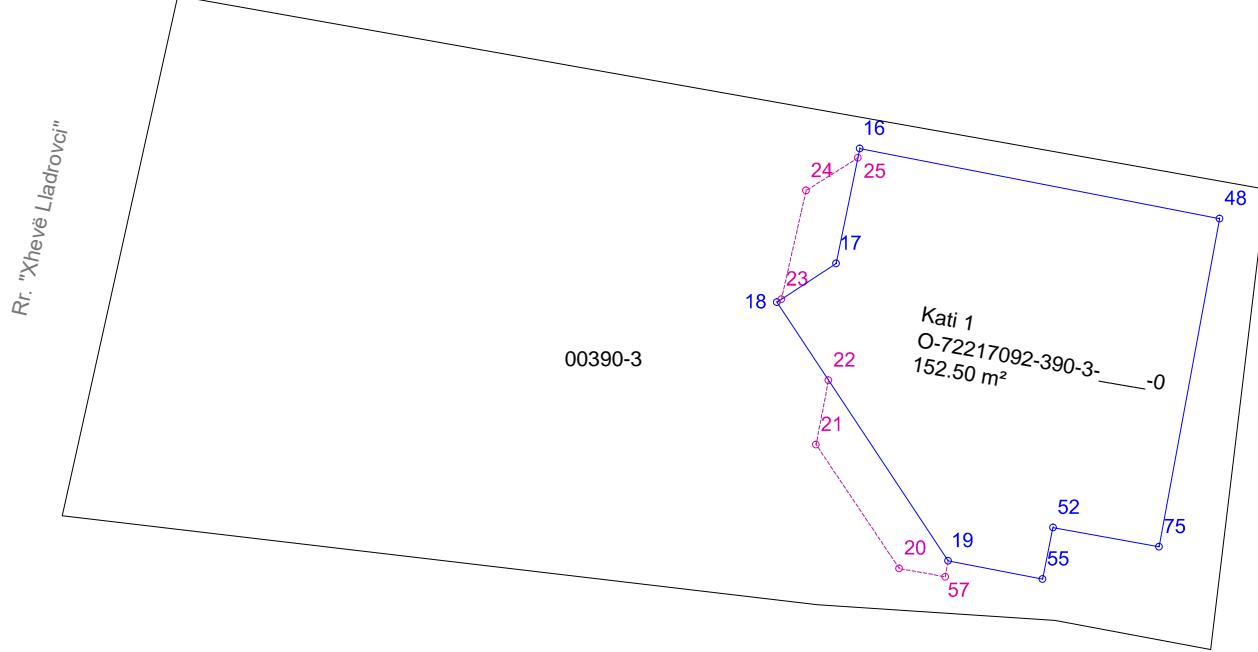

Nr.	Y	X	H	D	Etazhi	Sqarim	Sipërfaqja (m ²)
16	7512567.71	4693420.51	625.88	katil	Kati 1	Kati 1	137.65
17	7512566.93	4693416.72	625.88	katil			
18	7512564.97	4693415.43	625.88	katil			
19	7512570.63	4693406.88	625.88	katil			
48	7512579.60	4693418.19	625.88	katil			
52	7512574.10	4693407.98	625.88	katil			
55	7512573.75	4693406.28	625.88	katil			
75	7512577.61	4693407.35	625.88	katil			
20	7512569.02	4693406.63	625.88	katil-terasa		Terasa	9.49
21	7512566.26	4693410.73	625.88	katil-terasa			
22	7512566.68	4693412.86	625.88	katil-terasa			
23	7512565.12	4693415.53	625.88	katil-terasa		Terasa	5.36
24	7512565.94	4693419.12	625.88	katil-terasa			
25	7512567.64	4693420.20	625.88	katil-terasa			
57	7512570.53	4693406.36	625.88	katil-terasa		Gjithsej:	152.50

Rilevoi / Snimio: LIRIDON SEJDIU
(emri dhe mbiemri i gjydetit/kompanisë/ ime i prezime geodeta/ kompanije)Aprovoi / Usvojio: _____
(emri dhe mbiemri i pësonit zyrtar/ ime i prezime sluzbeneg lica)Nr. i licencës / Br. licence: 140

V.V.

Nënshkrimi / Potpis: _____

Nënshkrimi / Potpis: _____

Data e rilevimit / Datum snimanja: 04.09.2025

Data e rilevimit / Datum snimanja: _____

Zyra kadastrale komunale / Opštinska katastarska kancelarija: FerizajNr. i njësisë kadastrale / Br. katastarske jedinice : 00390-3Zona kadastrale / Katastarska zona: Ferizaj

Numri i lëndës / Broj predmeta: _____


Lloji i njësisë kadastrale / Vrsta katastarske jedinice : ShtëpiShkalla e zvoglimit / Razmera plana 1: 250**Republika e Kosovës****Republika Kosova-Republic of Kosovo****Qeveria -Vlada-Government****Ministria e Mjedisit dhe Planifikimit Hapësinor /Ministarstvo Sredine i Prostornog Planiranja/Ministry of Environment and Spatial Planning**

AGJENCIA KADASTRALE E KOSOVËS/KATASTARSKA AGECIJA KOSOVA/KOSOVA CADASTRAL AGENCY



Rr. "Xhevë Lladrovci"

00390-3

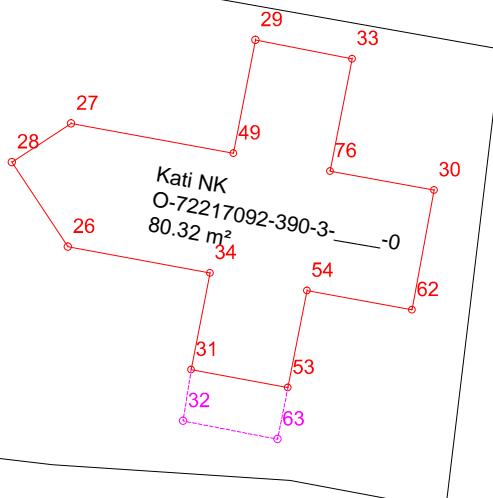

Nr.	Y	X	H	D	Etazhi	Sqarim	Sipërfaqja (m ²)
26	7512566.82	4693412.64	629.13	Nenkulmi	Kati Nk	Kati Nk	74.77
27	7512566.93	4693416.72	629.13	Nenkulmi			
28	7512564.97	4693415.43	629.13	Nenkulmi			
29	7512573.02	4693419.48	629.13	Nenkulmi			
30	7512578.93	4693414.51	629.13	Nenkulmi			
31	7512570.90	4693408.58	629.13	Nenkulmi			
33	7512576.21	4693418.85	629.13	Nenkulmi			
34	7512571.52	4693411.78	629.13	Nenkulmi			
49	7512572.29	4693415.73	629.13	Nenkulmi			
53	7512574.10	4693407.98	629.13	Nenkulmi			
54	7512574.72	4693411.19	629.13	Nenkulmi			
62	7512578.20	4693410.55	629.13	Nenkulmi			
76	7512575.49	4693415.14	629.13	Nenkulmi			
32	7512570.63	4693406.88	629.13	nenkulmi-terasa	Terasa		5.56
63	7512573.75	4693406.28	629.13	nenkulmi-terasa		Gjithsej:	80.32

Rilevoi / Snimio: LIRIDON SEJDIU
(emri dhe mbiemri i gjyqetit/kompanisë/ ime i prezime geodeta/ kompanije)Aprovoi / Usvojio: _____
(emri dhe mbiemri i pësonit zyrtar/ ime i prezime sluzbeneg lica)Nr. i licencës / Br. licence: 140

V.V.

Nënshkrimi / Potpis: _____

Nënshkrimi / Potpis: _____

Data e rilevimit / Datum snimanja: 04.09.2025

Data e rilevimit / Datum snimanja: _____



Republika e Kosovës

Republika Kosova-Republic of Kosovo

Geveria e Kosovës- Vlada Kosova- Government of Kosovo

Ministria e Infrastrukturës dhe Ambientit/ Ministrastvo Infrastrukture i Sredine/ Ministry of Infrastructure and Environment

AGJENCIA KADASTRALE E KOSOVËS/KOSOVSKA KATASTARSKA AGENCIJA/ KOSOVO CADASTRAL AGENCY

Komuna: Ferizaj

Numri i njësis kadastrale: 00390-3

Zona Kadastrale: Ferizaj

Sistemi koordinat: KosovaRef01

Nr.	Y	X	H	D	Etazhi	Sqarim	Sipërfaqja (m ²)
8	7512567.71	4693420.51	623.25	perdhese	Përdhesa	Përdhesa	140.46
9	7512566.82	4693412.64	623.25	perdhese			
10	7512566.46	4693410.96	623.25	perdhese			
11	7512567.64	4693409.13	623.25	perdhese			
12	7512566.93	4693416.72	623.25	perdhese			
13	7512564.96	4693415.43	623.25	perdhese			
14	7512570.90	4693408.58	623.25	perdhese			
15	7512570.63	4693406.88	623.25	perdhese			
47	7512579.60	4693418.19	623.25	perdhese			
50	7512577.61	4693407.35	623.25	perdhese			
51	7512574.10	4693407.98	623.25	perdhese			
56	7512573.75	4693406.28	623.25	perdhese			
						Gjithsej:	140.46

Nr.	Y	X	H	D	Etazhi	Sqarim	Sipërfaqja (m ²)
8	7512567.71	4693420.51	620.54	Bodrumi	Bodrumi	Bodrumi	140.46
9	7512566.82	4693412.64	620.54	Bodrumi			
10	7512566.46	4693410.96	620.54	Bodrumi			
11	7512567.64	4693409.13	620.54	Bodrumi			
12	7512566.93	4693416.72	620.54	Bodrumi			
13	7512564.96	4693415.43	620.54	Bodrumi			
14	7512570.90	4693408.58	620.54	Bodrumi			
15	7512570.63	4693406.88	620.54	Bodrumi			
47	7512579.60	4693418.19	620.54	Bodrumi			
50	7512577.61	4693407.35	620.54	Bodrumi			
51	7512574.10	4693407.98	620.54	Bodrumi			
56	7512573.75	4693406.28	620.54	Bodrumi			
						Gjithsej:	140.46

Nr.	Y	X	H	D	Etazhi	Sqarim	Sipërfaqja (m ²)
16	7512567.71	4693420.51	625.88	katil	Kati 1	Kati 1	137.65
17	7512566.93	4693416.72	625.88	katil			
18	7512564.97	4693415.43	625.88	katil			
19	7512570.63	4693406.88	625.88	katil			
48	7512579.60	4693418.19	625.88	katil			
52	7512574.10	4693407.98	625.88	katil			
55	7512573.75	4693406.28	625.88	katil			
75	7512577.61	4693407.35	625.88	katil			
20	7512569.02	4693406.63	625.88	katil-terasa		Terasa	9.49
21	7512566.26	4693410.73	625.88	katil-terasa			
22	7512566.68	4693412.86	625.88	katil-terasa			
23	7512565.12	4693415.53	625.88	katil-terasa		Terasa	5.36
24	7512565.94	4693419.12	625.88	katil-terasa			
25	7512567.64	4693420.20	625.88	katil-terasa			
57	7512570.53	4693406.36	625.88	katil-terasa		Gjithsej:	152.50

Nr.	Y	X	H	D	Etazhi	Sqarim	Sipërfaqja (m ²)
26	7512566.82	4693412.64	629.13	Nenkulmi	Kati Nk	Kati Nk	74.77
27	7512566.93	4693416.72	629.13	Nenkulmi			
28	7512564.97	4693415.43	629.13	Nenkulmi			
29	7512573.02	4693419.48	629.13	Nenkulmi			
30	7512578.93	4693414.51	629.13	Nenkulmi			
31	7512570.90	4693408.58	629.13	Nenkulmi			
33	7512576.21	4693418.85	629.13	Nenkulmi			
34	7512571.52	4693411.78	629.13	Nenkulmi			
49	7512572.29	4693415.73	629.13	Nenkulmi			
53	7512574.10	4693407.98	629.13	Nenkulmi			
54	7512574.72	4693411.19	629.13	Nenkulmi			
62	7512578.20	4693410.55	629.13	Nenkulmi			
76	7512575.49	4693415.14	629.13	Nenkulmi			
32	7512570.63	4693406.88	629.13	nenkulmi-terasa		Terasa	5.56
63	7512573.75	4693406.28	629.13	nenkulmi-terasa		Gjithsej:	80.32

Gjeodeti / Kompania gjeodete e licencuar:	Liridon Sejdiu	Nënshkrimi dhe vula:	
Numri i licencës	140		




Republika e Kosovës
Republika Kosova-Republic of Kosovo
Qeveria -Vlada-Government

*Ministria e Mjedisit dhe Planifikimit Hapësinor /Ministarstvo Sredine i Prostornog Planiranja/Ministry of Environment and Spatial Planning
AGJENCIA KADASTRALE E KOSOVËS/KATASTARSKA AGECIJA KOSOVA/KOSOVA CADASTRAL AGENCY*



Rr. "Xheivë Lladrovci"

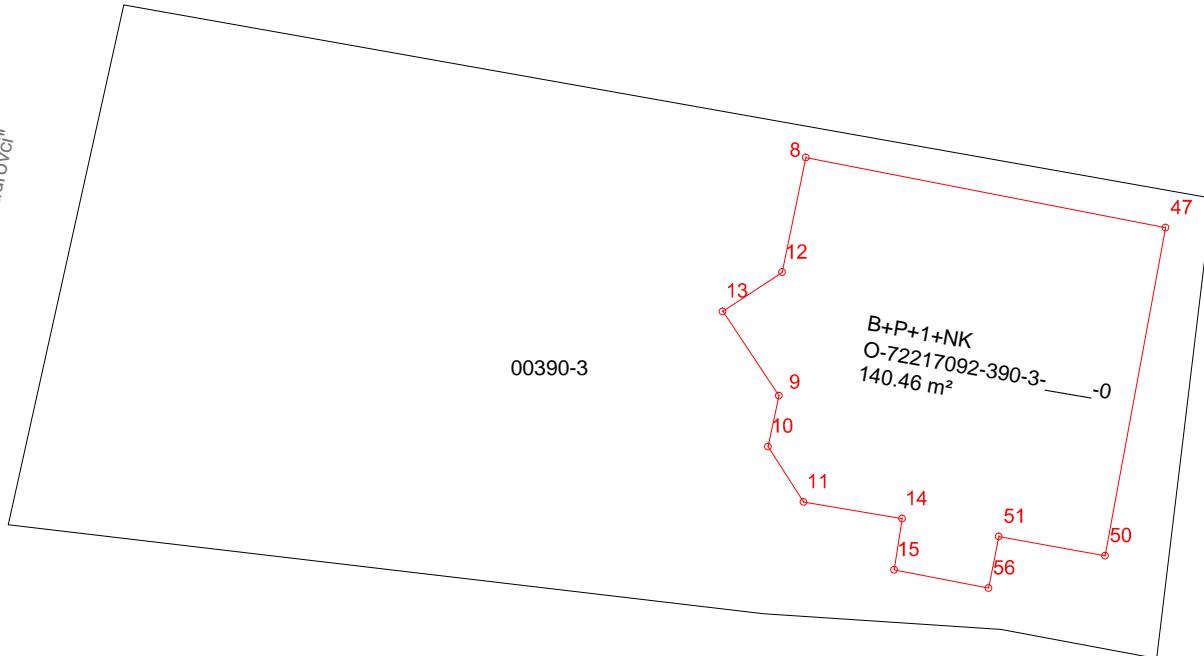

Nr	Y	X	H	Kodi	Përshkrimi	Burimi
8	7512567.708	4693420.511	623.250	40	Shtëpi-Ndërtesë	PM
9	7512566.818	4693412.642	623.250	40	Shtëpi-Ndërtesë	PM
10	7512566.458	4693410.963	623.250	40	Shtëpi-Ndërtesë	PM
11	7512567.639	4693409.133	623.250	40	Shtëpi-Ndërtesë	PM
12	7512566.927	4693416.722	623.250	40	Shtëpi-Ndërtesë	PM
13	7512564.962	4693415.429	623.250	40	Shtëpi-Ndërtesë	PM
14	7512570.896	4693408.576	623.250	40	Shtëpi-Ndërtesë	PM
15	7512570.628	4693406.883	623.250	40	Shtëpi-Ndërtesë	PM
47	7512579.602	4693418.194	623.250	40	Shtëpi-Ndërtesë	PM
50	7512577.609	4693407.345	623.250	40	Shtëpi-Ndërtesë	PM
51	7512574.097	4693407.982	623.250	40	Shtëpi-Ndërtesë	PM
56	7512573.750	4693406.277	623.250	40	Shtëpi-Ndërtesë	PM

Rilevoi / Snimio: LIRIDON SEJDIU
(emri dhe mbiemri i gjyqetit/kompanisë/ ime i prezime geodeta/ kompanije)Aprovoi / Usvojio: _____
(emri dhe mbiemri i pësonit zyrtar/ ime i prezime sluzbeneg lica)Nr. i licencës / Br. licence: 140

V.V.

Nënshkrimi / Potpis: _____

Nënshkrimi / Potpis: _____

Data e rilevimit / Datum snimanja: 04.09.2025

Data e rilevimit / Datum snimanja: _____



Republika e Kosovës
Republika Kosova-Republic of Kosovo
Qeveria e Kosovës- Vlada Kosova- Government of Kosovo
Ministria e Infrastrukturës dhe Ambientit/ Ministrastvo Infrastrukture i Sredine/ Ministry of Infrastructure and Environment
AGJENCIA KADASTRALE E KOSOVËS/KOSOVSKA KATASTARSKA AGENCIJA/ KOSOVO CADASTRAL AGENCY

Komuna: Ferizaj

Numri i njësis kadastrale: 00390-3

Zona Kadastrale: Ferizaj

Sistemi koordinat: KosovaRef01

Nr	Y	X	H	Kodi	Përshkrimi	Burimi
8	7512567.708	4693420.511	623.250	40	Shtëpi-Ndërtesë	PM
9	7512566.818	4693412.642	623.250	40	Shtëpi-Ndërtesë	PM
10	7512566.458	4693410.963	623.250	40	Shtëpi-Ndërtesë	PM
11	7512567.639	4693409.133	623.250	40	Shtëpi-Ndërtesë	PM
12	7512566.927	4693416.722	623.250	40	Shtëpi-Ndërtesë	PM
13	7512564.962	4693415.429	623.250	40	Shtëpi-Ndërtesë	PM
14	7512570.896	4693408.576	623.250	40	Shtëpi-Ndërtesë	PM
15	7512570.628	4693406.883	623.250	40	Shtëpi-Ndërtesë	PM
47	7512579.602	4693418.194	623.250	40	Shtëpi-Ndërtesë	PM
50	7512577.609	4693407.345	623.250	40	Shtëpi-Ndërtesë	PM
51	7512574.097	4693407.982	623.250	40	Shtëpi-Ndërtesë	PM
56	7512573.750	4693406.277	623.250	40	Shtëpi-Ndërtesë	PM

Gjeodeti / Kompania gjeodete e licencuar:	Liridon Sejdiu	Nënshkrimi dhe vula:	
Numri i licencës	140		



Republika e Kosovës

Republika Kosova - Republic of Kosovo

Qeveria e Kosovës - Vlada Kosova - Government of Kosovo

Ministria e Infrastrukturës dhe Ambientit/ Ministrastvo Infrastrukture i Sredine/ Ministry of Infrastructure and Environment

AGJENCIA KADASTRALE E KOSOVËS/ KOSOVSKA KATASTARSKA AGENCIJA/ KOSOVA CADASTRAL AGENCY

R E G J I S T R I M I I N DERTESËS / SHTËPISË													
Nr	Komuna	Zona Kadastrale	Numri i ndërtesës (njësia)	Etazhitëti	Katet	Sipërfaqja e kateve [m ²]	Sipërfaqja e bazamentit [m ²]	Adresa e Njësisë	Vendi i quajtur	Shfrytëzimi i aktual	Pronari / Shfrytëzuesi Emri (Emri i prindit) Mbiemri	Numri përsnal	Pjesa e Pronës
1	Ferizaj	Ferizaj	O-72217092-_____0	B+P+1+Nk	Bodrumi Përdhesa Kati 1 Kati NK Gjithsej:	140.46 140.46 152.50 80.32 513.74	140.46	Rr. "Xhevë Lladrovci"	LAMET	Banim	Bafti (Zeqir) Alija	1030533808	1/1

Gjeodeti/kompania e licencuar: LIRIDON SEJDIU	Nr i licencës: 140	Nënshkrimi dhe vula:
---	--------------------	----------------------









